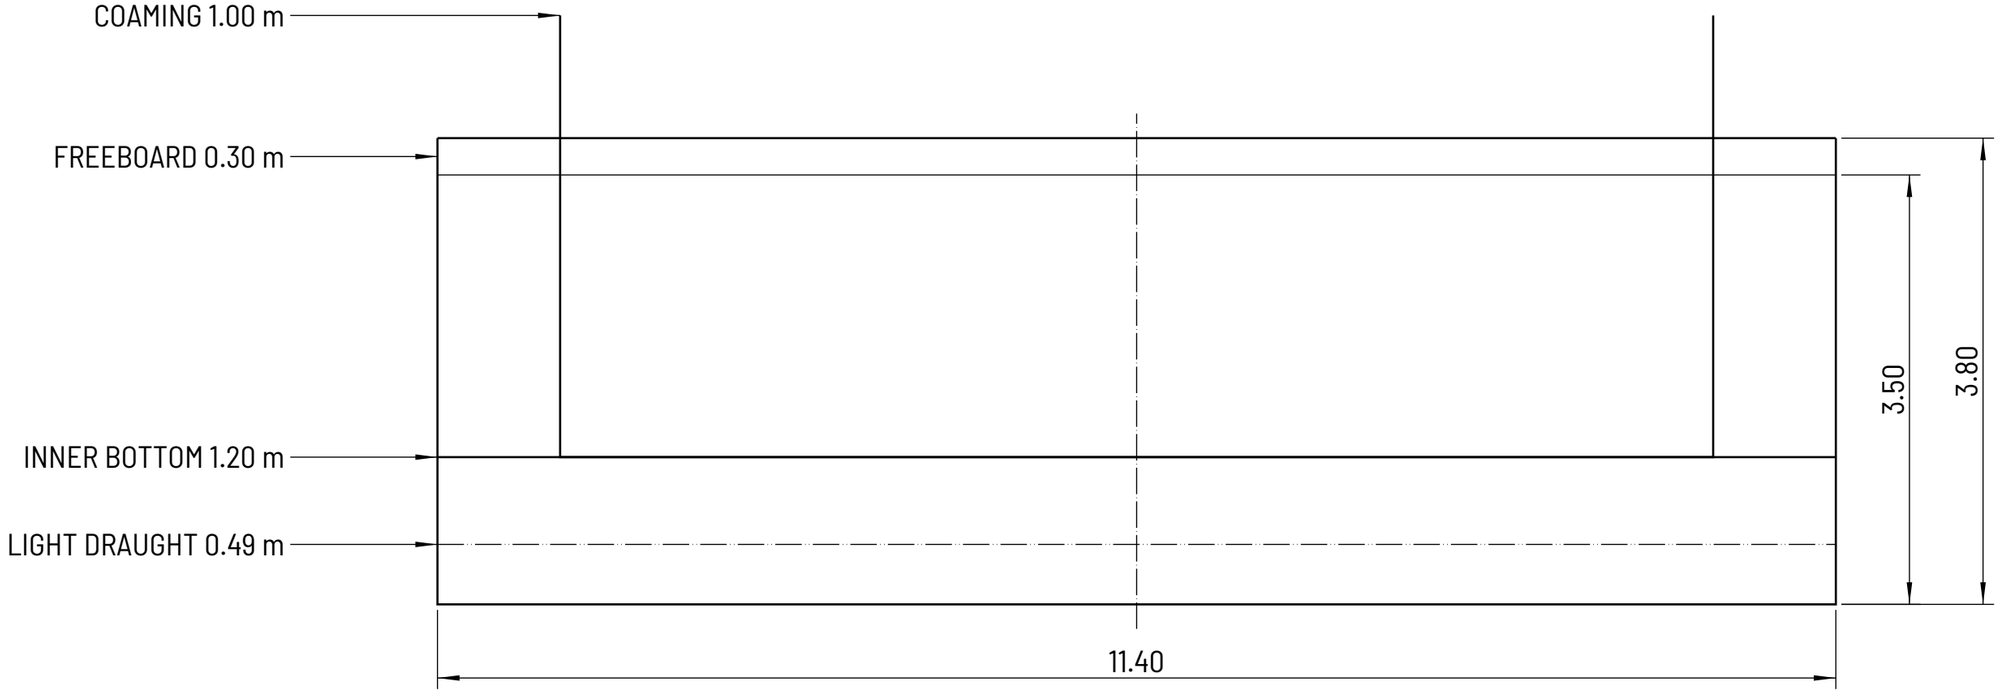


0 0.4 0.8 1.2 1.6 2 m
1:50

NOTES
1. MIDSHIP SECTION. DIMENSIONS IN METRES.
2. Box-hold dry bulk barge; Bauxite
CONCEPT – NOT FOR CONSTRUCTION